
# ΕΓΚΑΤΑΣΤΑΣΗ : ΗΛΕΚΤΡΟΛΟΓΙΚΗ
# ΘΕΣΗ : ΡΟΔΟΔΑΦΝΗΣ 13

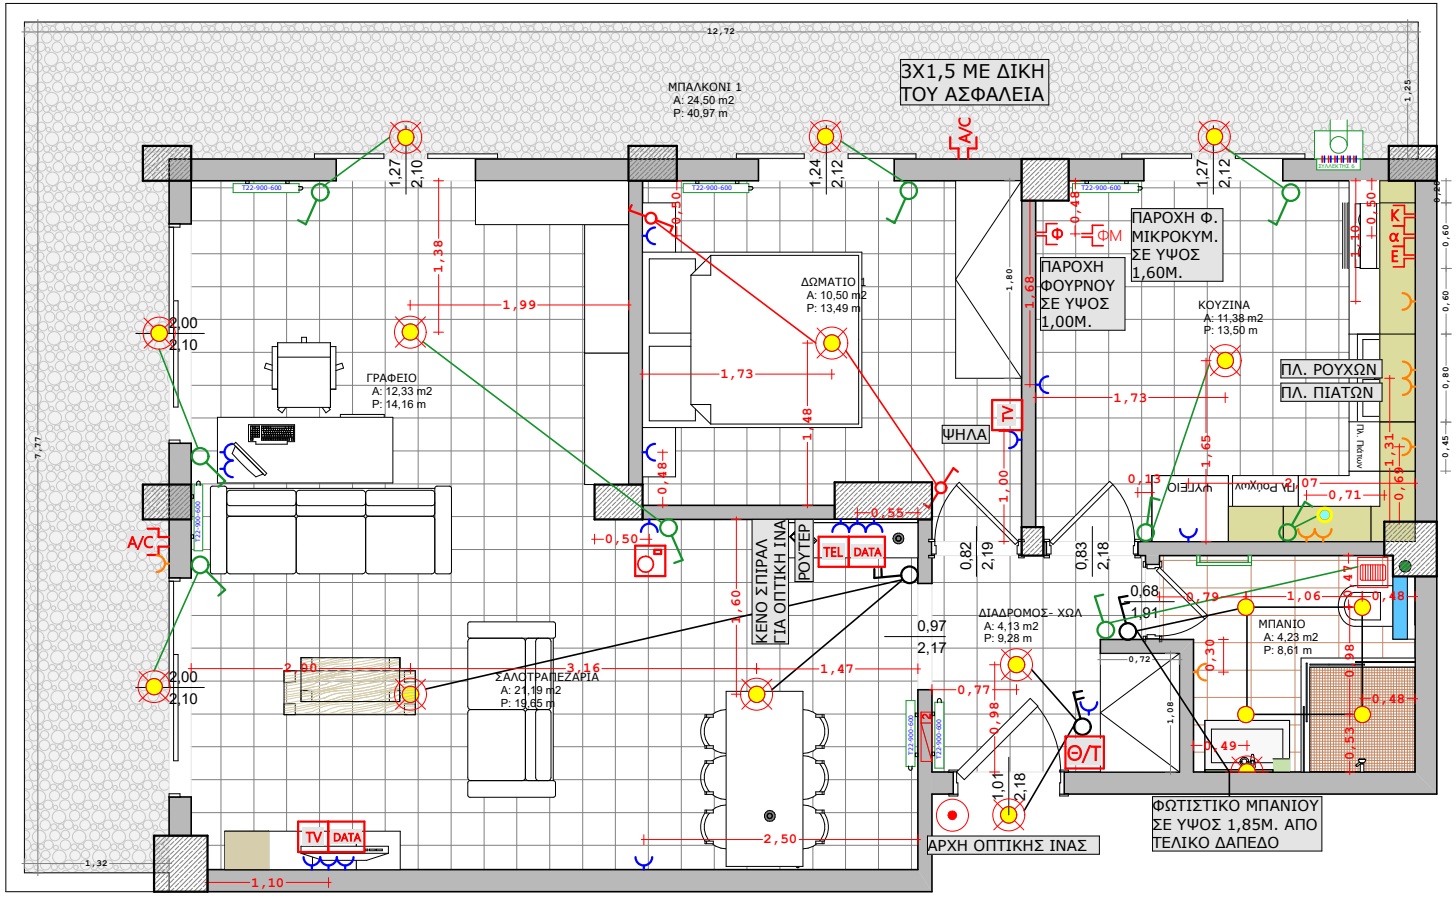


1) ΠΡΙΖΕΣ ΣΕ ΥΨΟΣ 0,55Μ. ΑΞΟΝΙΚΑ ΑΠΟ ΤΕΛΙΚΟ ΔΑΠΕΔΟ
2) ΠΡΙΖΕΣ ΠΑΓΚΟΥ ΚΟΥΖΙΝΑΣ ΣΕ ΥΨΟΣ 1,20 Μ. ΑΞΟΝΙΚΑ ΑΠΟ ΤΕΛΙΚΟ ΔΑΠΕΔΟ
3) ΠΡΙΖΑ ΜΠΑΝΙΟΥ 1,20Μ. ΑΞΟΝΙΚΑ ΑΠΟ ΤΕΛΙΚΟ ΔΑΠΕΔΟ
4) ΔΙΑΚΟΠΤΕΣ 1,25 Μ. ΑΞΟΝΙΚΑ ΑΠΟ ΤΕΛΙΚΟ ΔΑΠΕΔΟ
5) ΦΩΤΙΣΤΙΚΟ ΜΠΑΝΙΟΥ ΣΕ ΥΨΟΣ 1,85 Μ. ΑΠΟ ΤΕΛΙΚΟ ΔΑΠΕΔΟ
6) ΠΡΙΖΑ ΚΑΙ TV ΣΤΟ ΔΩΜΑΤΙΟ ΣΕ ΥΨΟΣ 1,60Μ. ΑΞΟΝΙΚΑ ΑΠΟ ΤΕΛΙΚΟ ΔΑΠΕΔΟ
7) ΟΤΑΝ ΕΧΟΥΜΕ ΠΛ. ΡΟΥΧΩΝ & ΠΙΑΤΩΝ ΣΤΗΝ ΚΟΥΖΙΝΑ ΝΑ ΑΦΗΝΟΥΝ ΝΥΜ 3*2,5 1Μ. ΜΕ ΦΙΣ ΣΤΗΝ ΑΚΡΗ
8) ΝΑ ΓΙΝΕΙ ΕΛΕΓΧΟΣ ΓΙΑ ΚΕΝΤΡΙΚΗ ΚΕΡΑΙΑ

| ΥΠΟΜΝΗΜΑ | |
|---|---|
| | Πρίζα 3Χ1,5 |
| | Πρίζα Ενισχυμένη 3Χ2,5 |
| | Διακόπτης μονός |
| | Διακόπτης διπλός |
| | Διακόπτης Αλε ρετούρ |
| | Διακόπτης Αλε ρετούρ - Διπλός Διακόπτης |
| 2 | Πίνακας 2 σειρών |
| | Spot |
| | LED |
| | Φώς |
| | Απλίκα |
| | Εξαερισμός |

| | |
|---|---|
| | Λέβητας Αερίου Επιτοίχιος |
| Φ | Φούρνος |
| ΦΜ | Φούρνος μικροκυμάτων |
| E | Εστίες |
| α | Απορροφητήρας |
| K | Παροχή Κουζίνας |
| A/C | Παροχή για Α/C |
| TV | Πρίζα Τηλεόρασης |
| TEL | Τηλέφωνο |
| DATA | DATA |
| | Θερμοστάτης χώρου |
| Θ/Τ | Θυροτηλέφωνο |
| | Κουδούνι |