
ΕΓΚΑΤΑΣΤΑΣΗ : ΥΔΡΑΥΛΙΚΗ
ΘΕΣΗ : ΡΟΔΟΔΑΦΝΗΣ 13

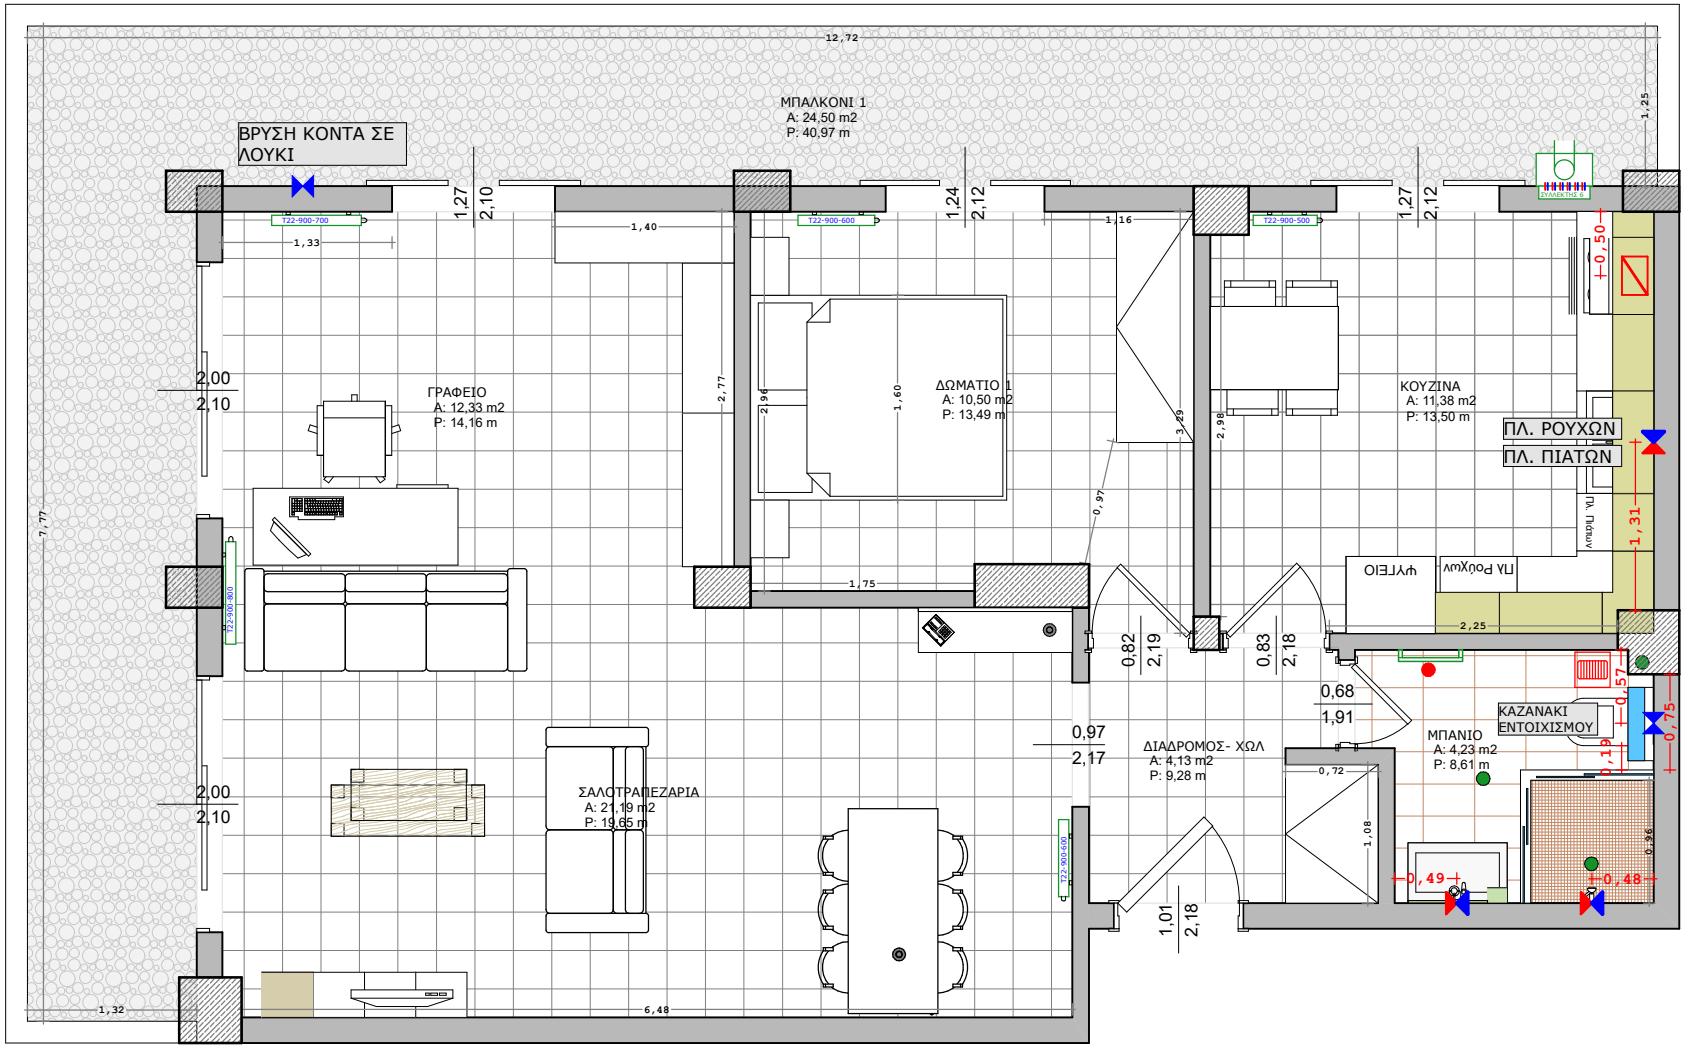

ΘΑ ΓΙΝΕΙ ΝΕΑ ΓΡΑΜΜΗ ΑΠΟ ΤΟ ΥΔΡΟΜΕΤΡΟ ΜΕΧΡΙ ΤΟ ΔΙΑΜΕΡΙΣΜΑ ΟΠΩΣ ΜΑΣ ΥΠΟΔΕΙΧΘΗΚΕ

ΥΠΟΜΝΗΜΑ	
	Παροχή κρύου & ζεστού νερού
	Παροχή κρύου νερού
	Απορροφητήρας
	Λέβητας Αερίου Επιτοίχιος
	Σιφώνι
	Κεντρική νερού